


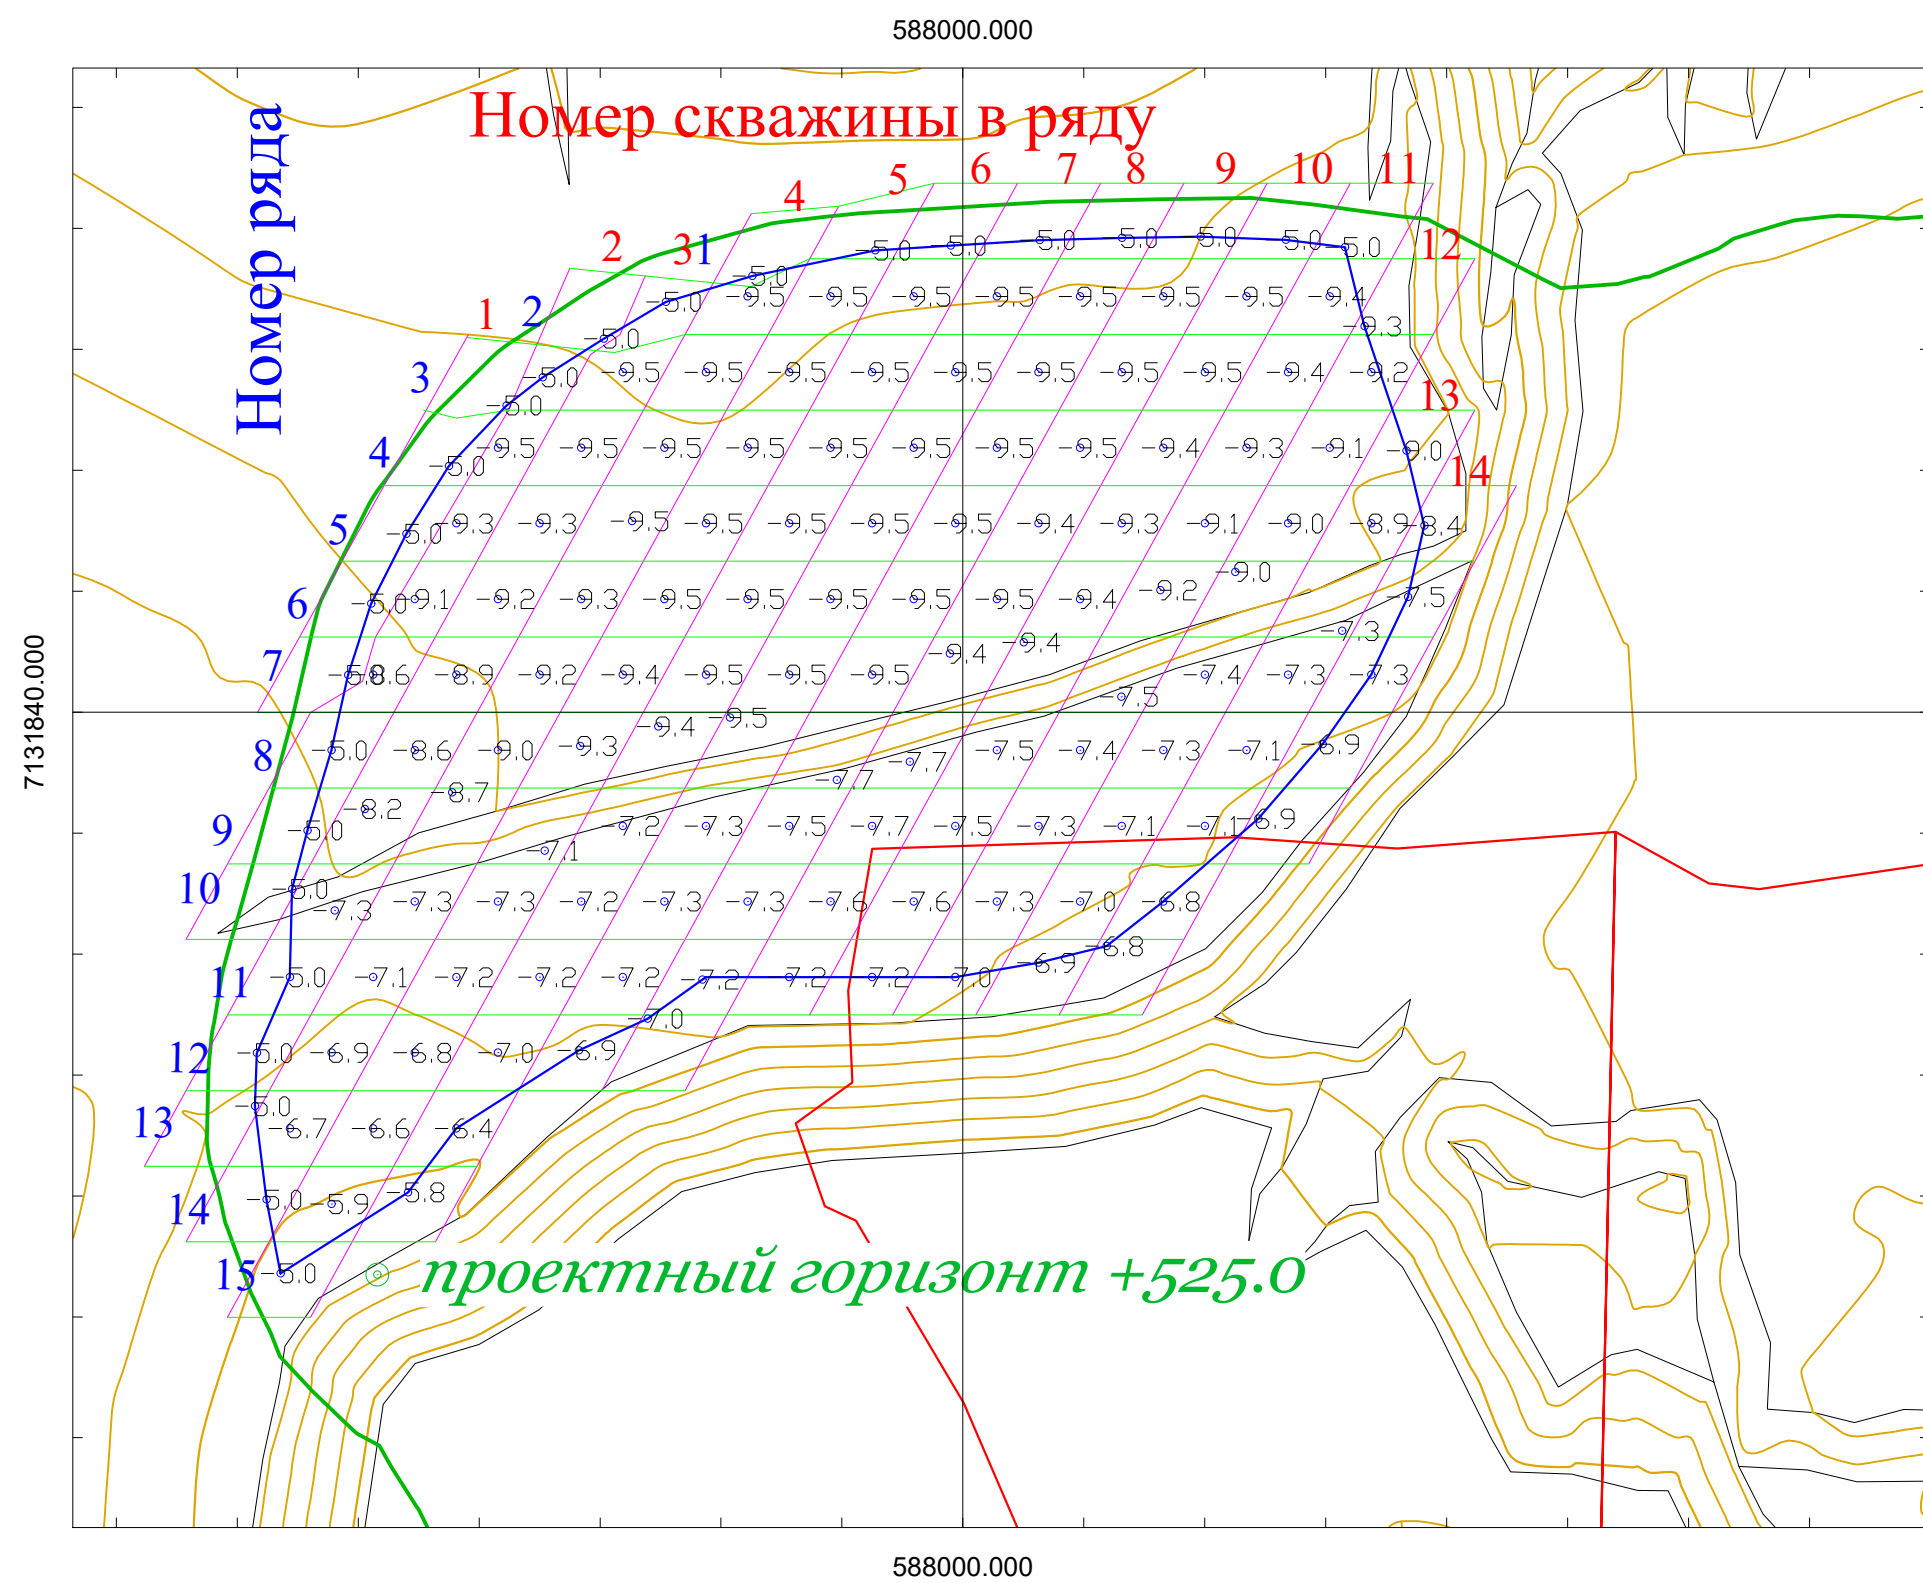

ПАСПОРТ
БУРОВЫХ РАБОТ
месторождение "Урочище Сайлык"
буровой блок П-15 (С₁-57)

"УТВЕРЖДАЮ"
Гл. инженер АО "Поиск Золото"
В.И. Парамонов
" " 2026г.

Примечание:

Буровой станок должен быть установлен на спланированной площадке уступа вне призмы обрушения и при бурении первого ряда расположен так, чтобы гусеницы станка находились от бровки уступа на расстоянии не менее чем 3 м, а его продольная ось была перпендикулярна бровке уступа.

Перемещение бурового станка с поднятой мачтой по уступу допускается только по спланированной горизонтальной площадке. При передвижении станка под линиями электропередачи мачта должна быть опущена.

При перегоне буровых станков мачта должна быть опущена, буровой инструмент снят или надежно закреплен. Устья скважины после окончания бурения должна быть очищена от бурового шлама и перекрыта.

Участки (блоки) пробуренных скважин ограждаются предупредительными знаками. При отбойке на подпорную стенку из ранее взорванной горной массы расчетный удельный расход ВВ на первых скважинах увеличить на 15-20%. С целью формирования более крутых углов откоса рабочих уступов блоков (левый торец полигона) вес зарядов в последних скважинах уменьшать на 10-15%.

Глубину скважин по блоку бурения контролирует геологическая служба АО "Поиск Золото".

Фактическую глубину бурения определяет маркшейдерская служба АО "Поиск Золото" в записью в журнал "Ежедневный контроль бурения"

Горизонт. + 525.0 м.


Консервацию скважин проводить согласно проекту " Консервации скважин на буровом блоке":

- установить в устье скважины защитный конус;
- обеспечить плотное перекрытие устья скважины конусом;

При отсутствии спец средств для консервации скважин, закрываем скважины мешковиной.

Технологические показатели П-15(ДМ45)			
№№ п/п	Наименование	Ед-ца изм.	Кол-во
1	Категория пород		V
2	Направление скважины	градус	90
3	Диаметр скважины	мм.	203
4	Площадь блока	т.м2	3,20
5	Средняя глубина скважины	м	7,8
6	Перебур	м	1,0
7	Расстояние между рядами	м	5,0
8	Расстояние между скважинами	м	5,5
9	КИС		0,9
10	Выход горной массы	т.м3	21,8
11	Сменная производительность	п.м.	300
12	Объем буровых работ	п.м.	1167
13	Количество скважин	шт.	149
C1- 57 = 149 шт;			
14	Время бурения блока	сутки	1,9

Проектная глубина скважин блок П15(ДМ45)														
Скв. №	1	2	3	4	5	6	7	8	9	10	11	12	13	14
Ряд.№														
1				5	5	5	5	5	5	5	5			
2		5	5	9,5	9,5	9,5	9,5	9,5	9,5	9,5	9,4	9,3		
3	5	5	9,5	9,5	9,5	9,5	9,5	9,5	9,5	9,5	9,4	9,2		
4	5	9,5	9,5	9,5	9,5	9,5	9,5	9,5	9,5	9,4	9,3	9,1	9	
5	5	9,3	9,3	9,5	9,5	9,5	9,5	9,5	9,4	9,3	9,1	9	8,9	8,4
6	5	9,1	9,2	9,3	9,5	9,5	9,5	9,5	9,5	9,4	9,2	9	7,3	7,5
7	5	8,6	8,9	9,2	9,4	9,5	9,5	9,5	9,4	9,4	7,5	7,4	7,3	7,3
8		5	8,6	9	9,3	9,4	9,5	7,7	7,7	7,5	7,4	7,3	7,1	6,9
9		5	8,2	8,7	7,1	7,2	7,3	7,5	7,7	7,5	7,3	7,1	7	6,9
10		5	7,3	7,3	7,3	7,2	7,3	7,3	7,6	7,6	7,3	7	6,8	
11			5	7,1	7,2	7,2	7,2	7,2	7,2	7,2	7	6,9	6,8	
12			5	6,9	6,8	7	6,9	7						
13			5	6,7	6,6	6,4								
14				5	5,9	5,8								
15					5,0									

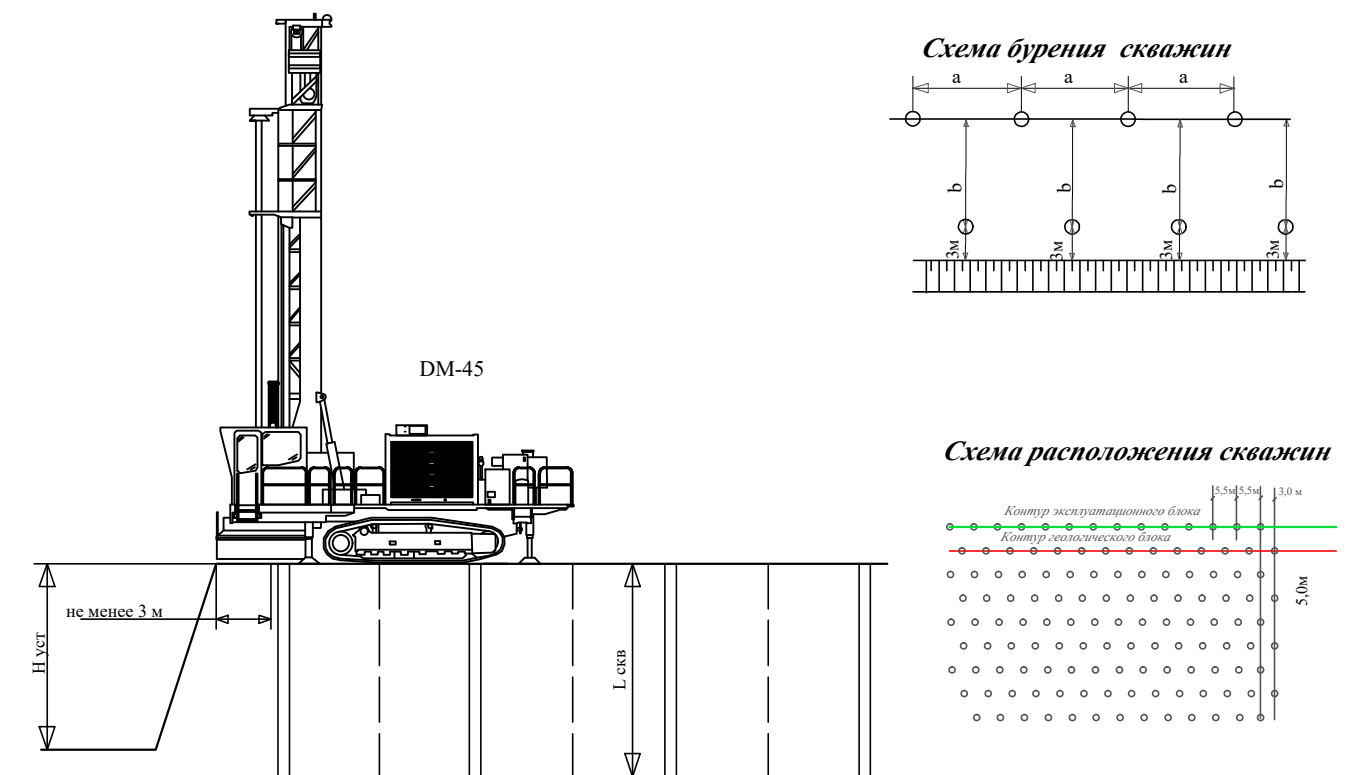

				Республика Саха (Якутия) Акционерное общество "Поиск Золото"	АО "Поиск Золото"	
Должность	Ф.И.О.	Подпись	Дата			
Гл. геолог	Помалейко А.А.			ПАСПОРТ буровых работ блока П-15 (первый слой)	Отдел	Масштаб
Гл. маркш-р	Ефимов С.Ф.				ПТО	1:750
Нач. УБВР	Сырбу Г.П.					
Нач. ПТО	Турчинскас В.И.					
Инж. ПТО	Маслова А.А.				Лист 1	Листов 1
				Месторождение "Урочище Сайлык " Блок С ₁ -57 (первый слой)		